


Nota:
Según el estudio de suelos detrás del fondo del lote se localiza una obra hidráulica de embalsamiento del drenaje local. Esto explica la mala calidad geotécnica del terreno fondo (relleno no controlado). Por datos topográficos la cota de este cañón es algo por debajo del nivel solar superior y por prevención se recomienda para las zapatas alineadas por el lindero fondo de la edificación (epi 1), garantizar una cota de cimentación por debajo de ese nivel.

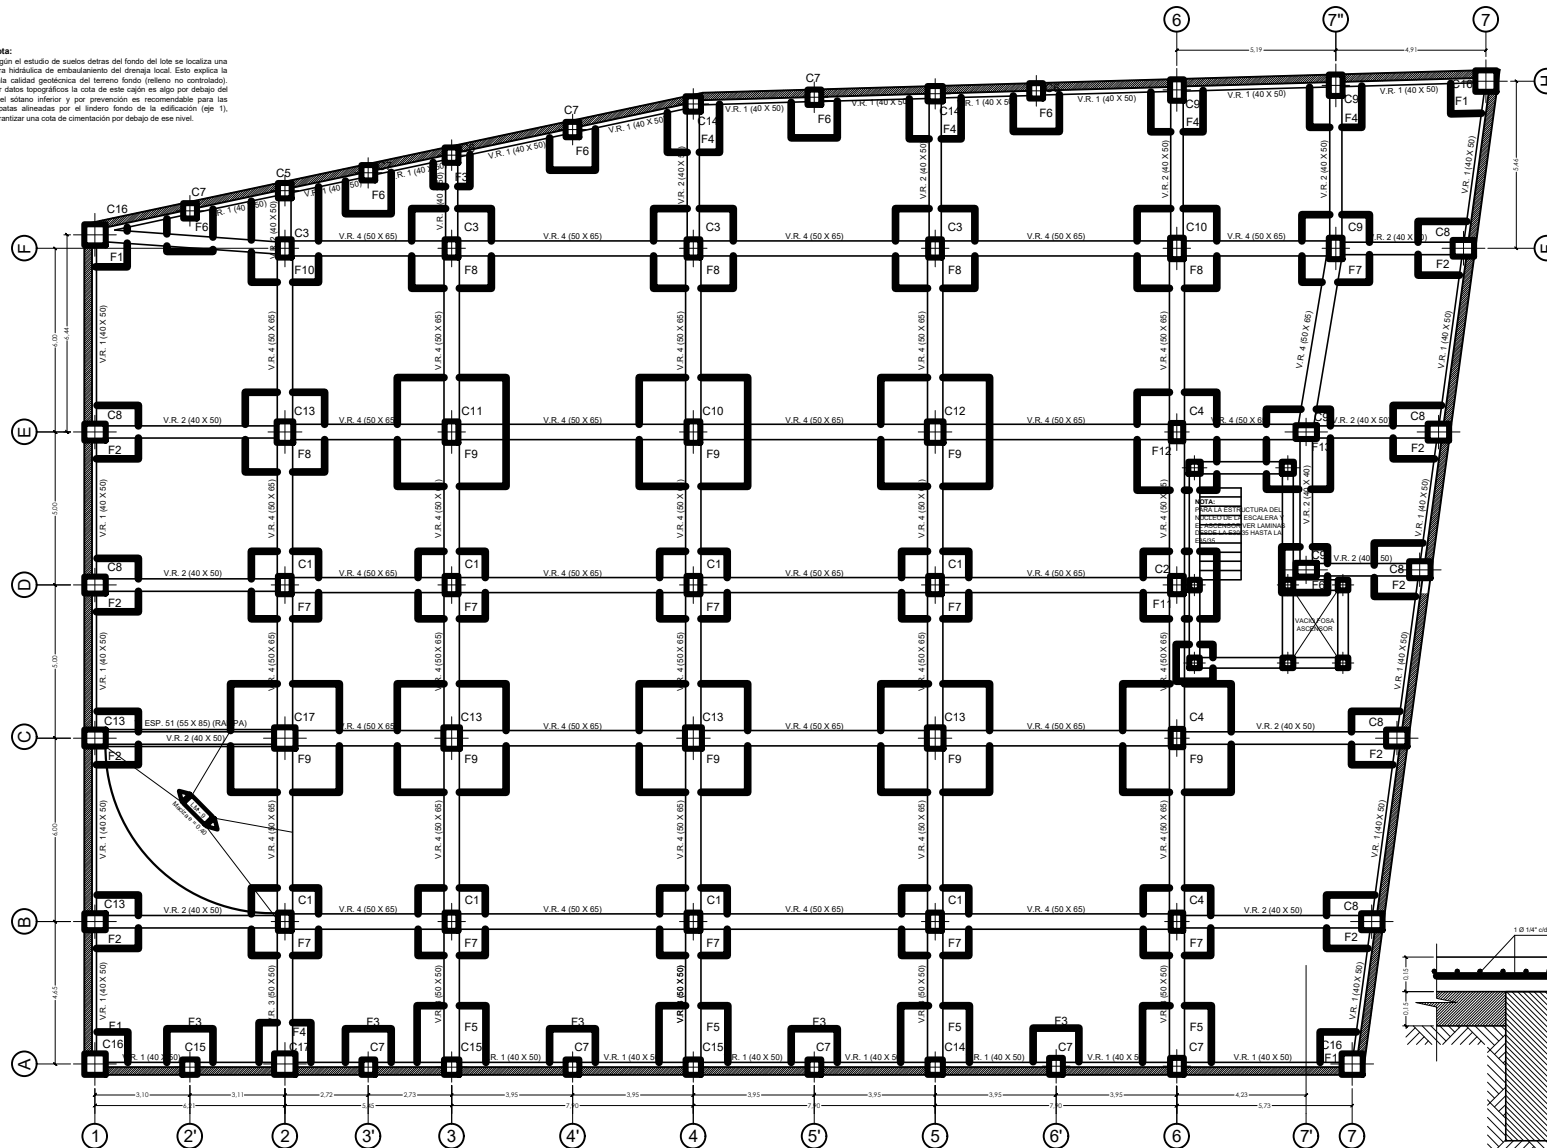

Planta índice fundaciones _____ Esc. 1: 75

DETALLE LOSA DE PISO _____ Esc. 1: 10



Geografía y Construcción
C.I. 9.218.667
Luis Mattheo Contreras
Arquitecto
C.I. 9.223.480 C.V. 15.294
Gestión Visual
Ingeniero
C.I. 9.207.869 C.V. 11.325

E-1/36

PROYECTO: SUPERMERCADO EXPRESS
Y OFICINAS CORPORATIVAS

CLIENTE: GARZÓN HIERMERCAO S.A.
UBICACIÓN: PASEO DEL COMERCIO, 2.º NIVEL, 4.00
MANTENIMIENTO: LA EMPRESA GARZÓN HIERMERCAO S.A.
FECHA: 01/03/2011
Escala: 1:75

